


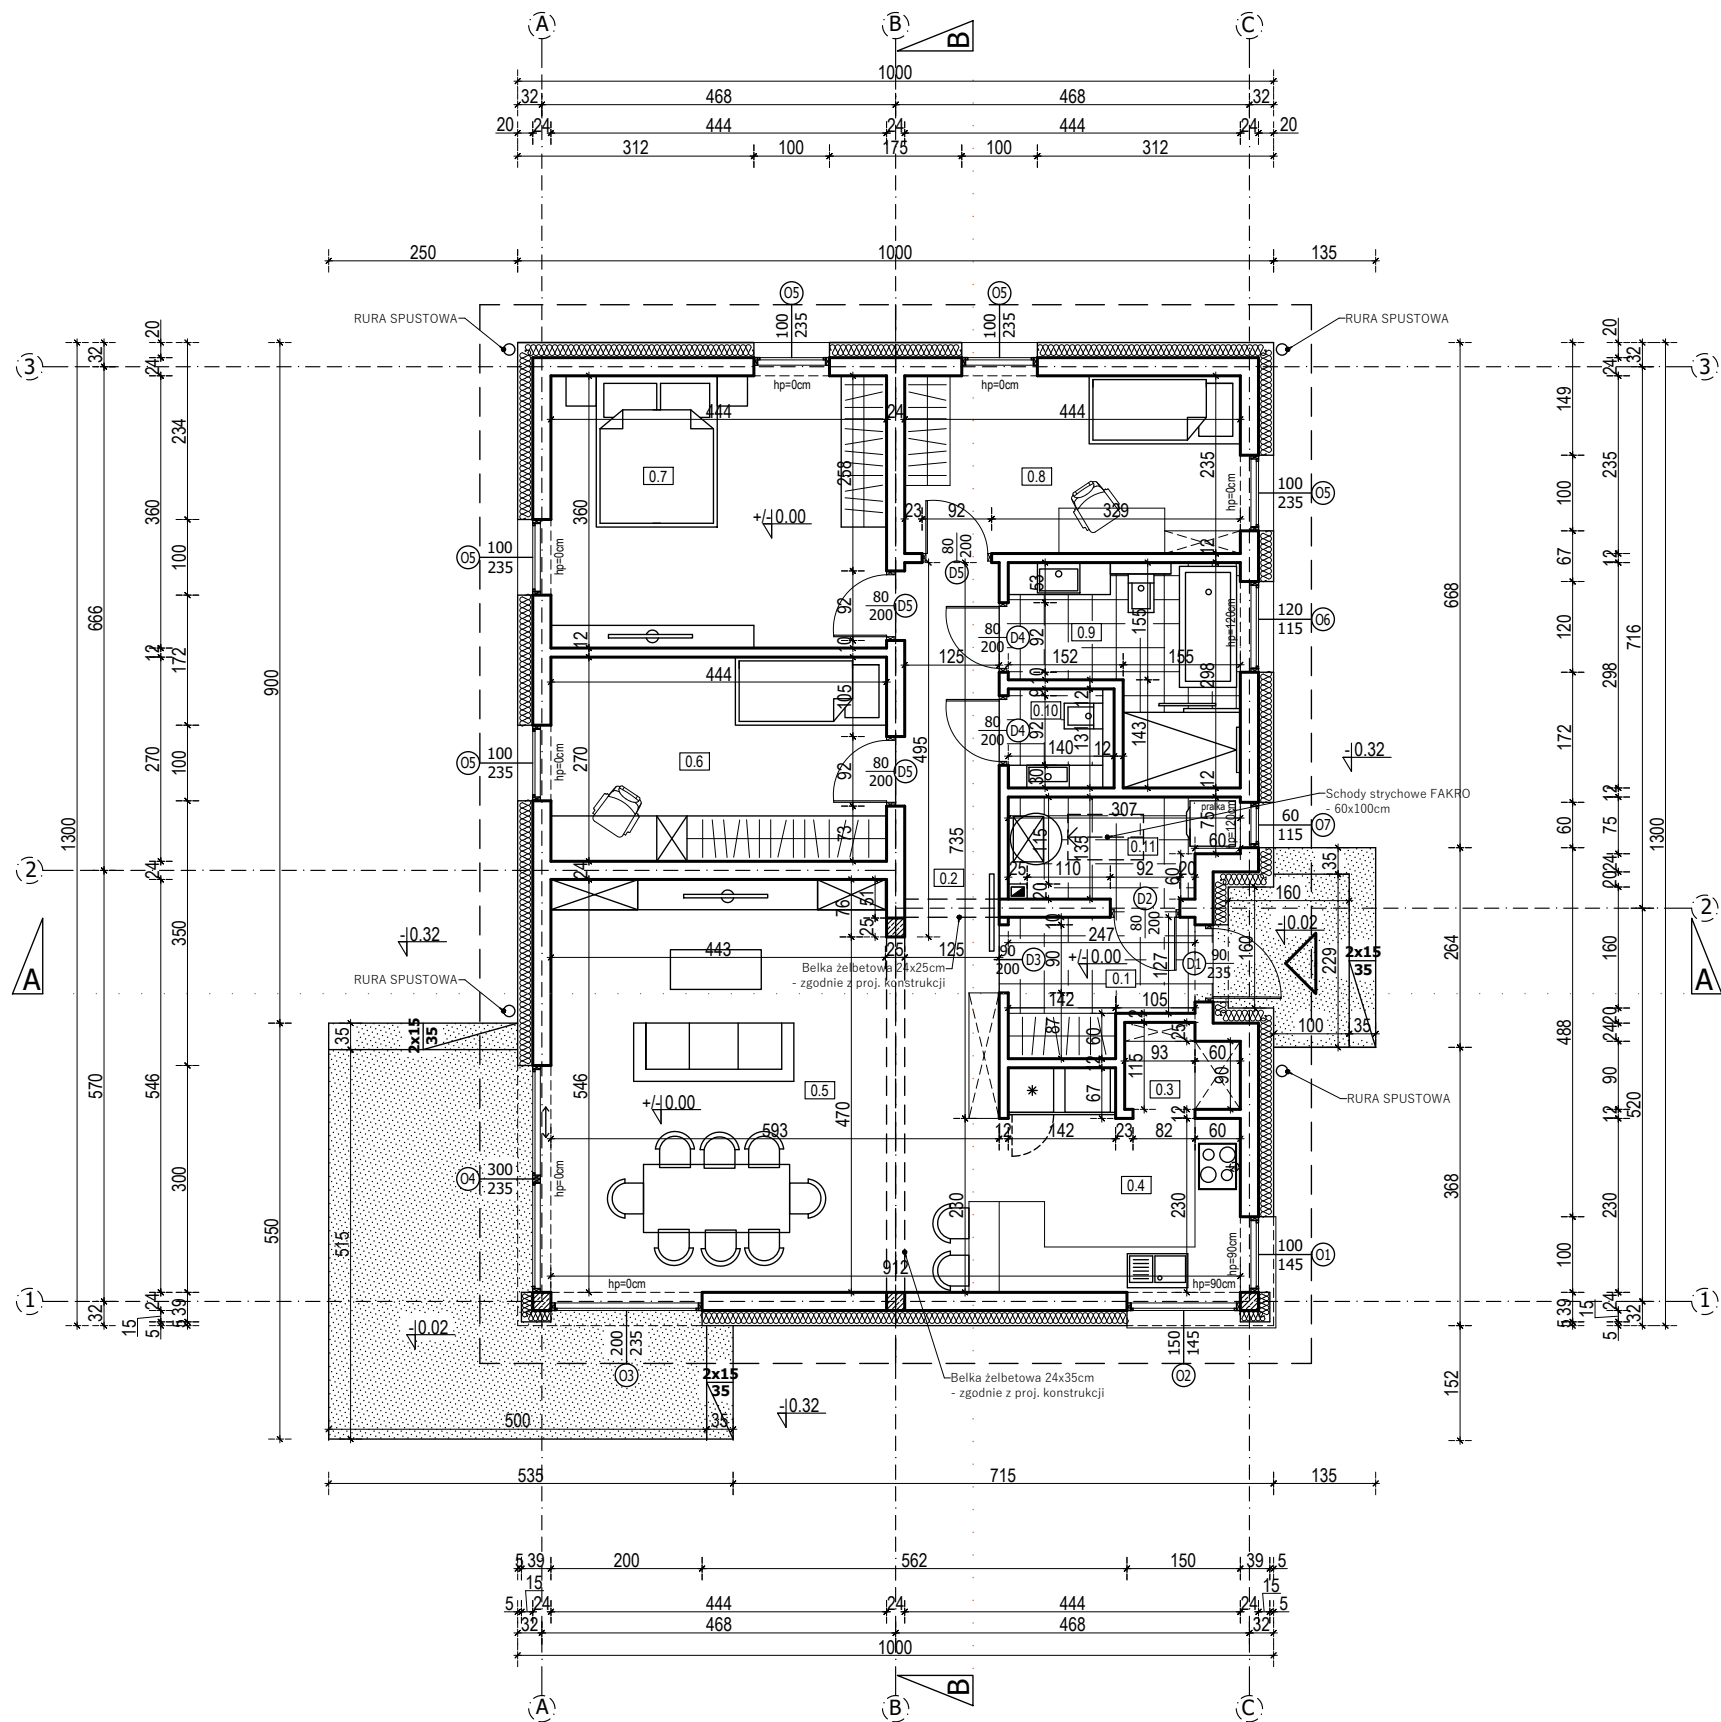

PARTER

L.P.	NAZWA POMIESZCZENIA	POWIERZCHNIA m ²	
		UŻYTKOWA	CAŁKOWITA
0.1	WIATROŁAP	4,00	4,00
0.2	KOMUNIKACJA	6,20	6,20
0.3	SPIŻARNIA	1,62	1,62
0.4	KUCHNIA	8,25	8,25
0.5	SALON	31,25	31,25
0.6	POKÓJ	11,97	11,97
0.7	SYPIALNIA	16,00	16,00
0.8	POKÓJ	10,43	10,43
0.9	ŁAZIENKA	9,97	9,97
0.10	WC	1,83	1,83
0.11	KOTŁOWNIA	-	3,78
SUMA		101,52	105,30

0.12	PODEST WEJŚCIOWY	18,00
0.13	TARAS	4,50
SUMA		22,50

UWAGI:

- Wszystkie elementy konstrukcyjne budynku (ściany, podłagi, stropy, elementy dachu: jętki, krokwie itp.) rozpatrywać łącznie z projektem konstrukcji, w przypadku stwierdzenia rozbieżności należy zwrócić się do projektanta celem wyjaśnienia.
- Rysunki rozpatrywać łącznie z częścią opisową oraz projektami pozostałych branż projektu technicznego, w przypadku stwierdzenia rozbieżności należy zwrócić się do projektanta celem wyjaśnienia.
- Wszystkie wymiary sprawdzić na budowie.

UWAGA:

Projekt budowlany został opracowany w stadium budowlanym w celu uzyskania pozwolenia na budowę. Projekt budowlany może stanowić podstawę do sporządzenia projektu wykonawczego na zlecenie inwestora. Zakres projektu wykonawczego powinien być ustalony i określony odrębną umową z projektantem na realizację takiej usługi. Opracowanie projektu wykonawczego nie jest obligatoryjne. Inwestor a także firma wykonawcza podejmuje odpowiedzialność za wprowadzane na budowie rozwiązania wykonawcze które są realizowane na etapie budowy na podstawie wyłącznie projektu budowlanego.

* UWAGA:

Układ warstw dachu należy dostosować do wymogów producenta blachy, biorąc pod uwagę w szczególności odpowiednie systemowe rozwiązania w zakresie prawidłowej wentylacji warstw wentylacyjnych pomiędzy blachą a membraną/folią wstępnego krycia a także wentylacji warstwy termoizolacji w przypadku stosowania warstw wstępnego krycia o dużym oporze dyfuzyjnym dla pary wodnej.

Należy zwrócić szczególną uwagę na prawidłowe rozwiązania dotyczące okapu dachu oraz gąsiora w kalenicy aby umożliwić odpowiednią wymianę powietrza w szczelinach wentylacyjnych.

Rozstaw łat należy dobrać odpowiednio dla konkretnego wybranego wariantu blachy kierując się przede wszystkim instrukcjami i zaleceniami producenta.

UWAGA:

wszystkie elementy konstrukcyjne budynku (ściany, podłagi, stropy, elementy dachu: jętki krokwie itp.) rozpatrywać łącznie z projektem konstrukcji, w przypadku stwierdzenia rozbieżności należy zwrócić się do projektanta celem wyjaśnienia.

WYMIARY STOLARKI:

ZEWNETRZNE -

- podano wymiary w świetle ościeży (otwór w ścianie w stanie surowym)

WEWNĘTRZNE -

- podano wymiary w świetle ościeżnicy (światło futryny drzwiowej)

NAZWA INWESTYCJI: BUDOWA BUDYNKU MIESZKALNEGO JEDNORODZINNEGO wraz z instalacjami: wod.-kan., c.o., elektryczna, gazowa, wentylacji mechanicznej z rekuperacją, ROZBIÓRKA I BUDOWA ODCINKA SIECI WODOCIĄGOWEJ		
TYTUŁ RYSUNKU: RZUT PARTERU	SKALA RYS.: 1:100	
Lokalizacja: PASZKÓWKA , działka nr ewid.: 2247/1 Jednostka ewid.: 121802_2 BRZEŹNICA Obręb ewid.: PASZKÓWKA 0010	FAZA OPRACOWANIA: PROJEKT ARCHITEKTONICZNO-BUDOWLANY	
JEDNOSTKA PROJEKTOWA: Dominika Spyрка ARCHITEKT	PROJEKTANT: ARCHITEKTURA mgr inż. arch. Dominika Spyрка upr. nr MPOIA/029/2018 w specjalności architektonicznej	NR RYS.: PAB 1
Ul. Krasińskiego 27/2 34-100 Wadowice kom. 518 191 515 adres e-mail: dominikaspyrkaarchitekt@gmail.com	PODPIS:	DATA OPRACOWANIA: 04.2024r. -02.2025r.